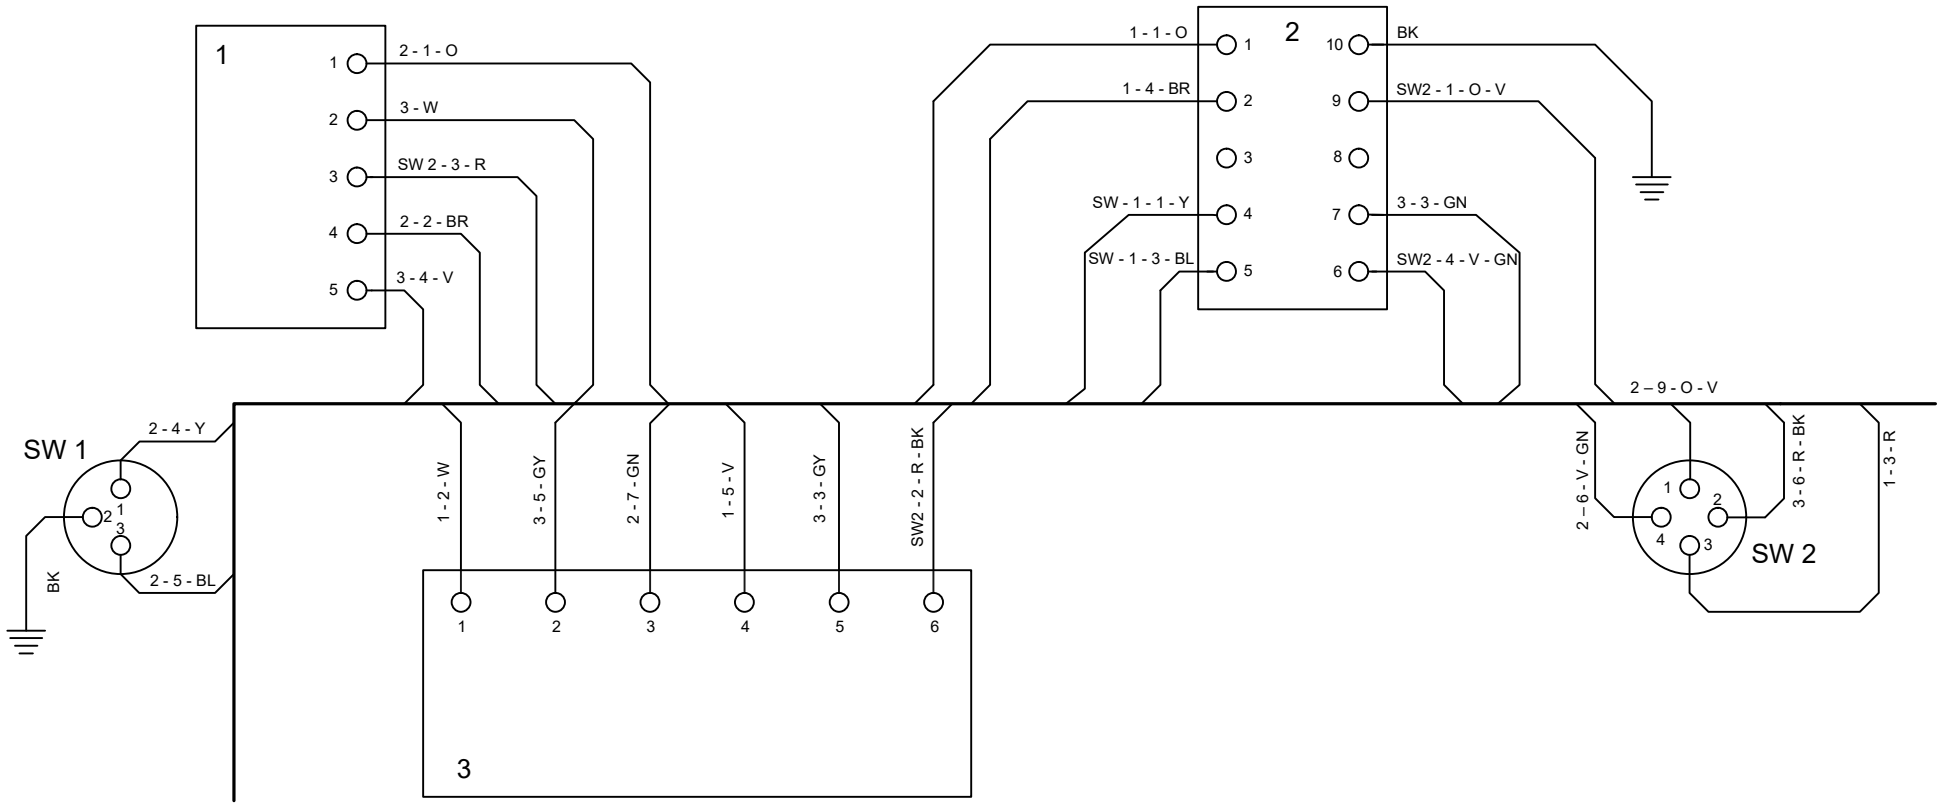


No. 11


DIAGRAM HIGHWAY

Prodi D3 Teknik Telekomunikasi

Nama : Devita Syifa A


Kelas : 1A TTE


Tgl. 9-04-2023

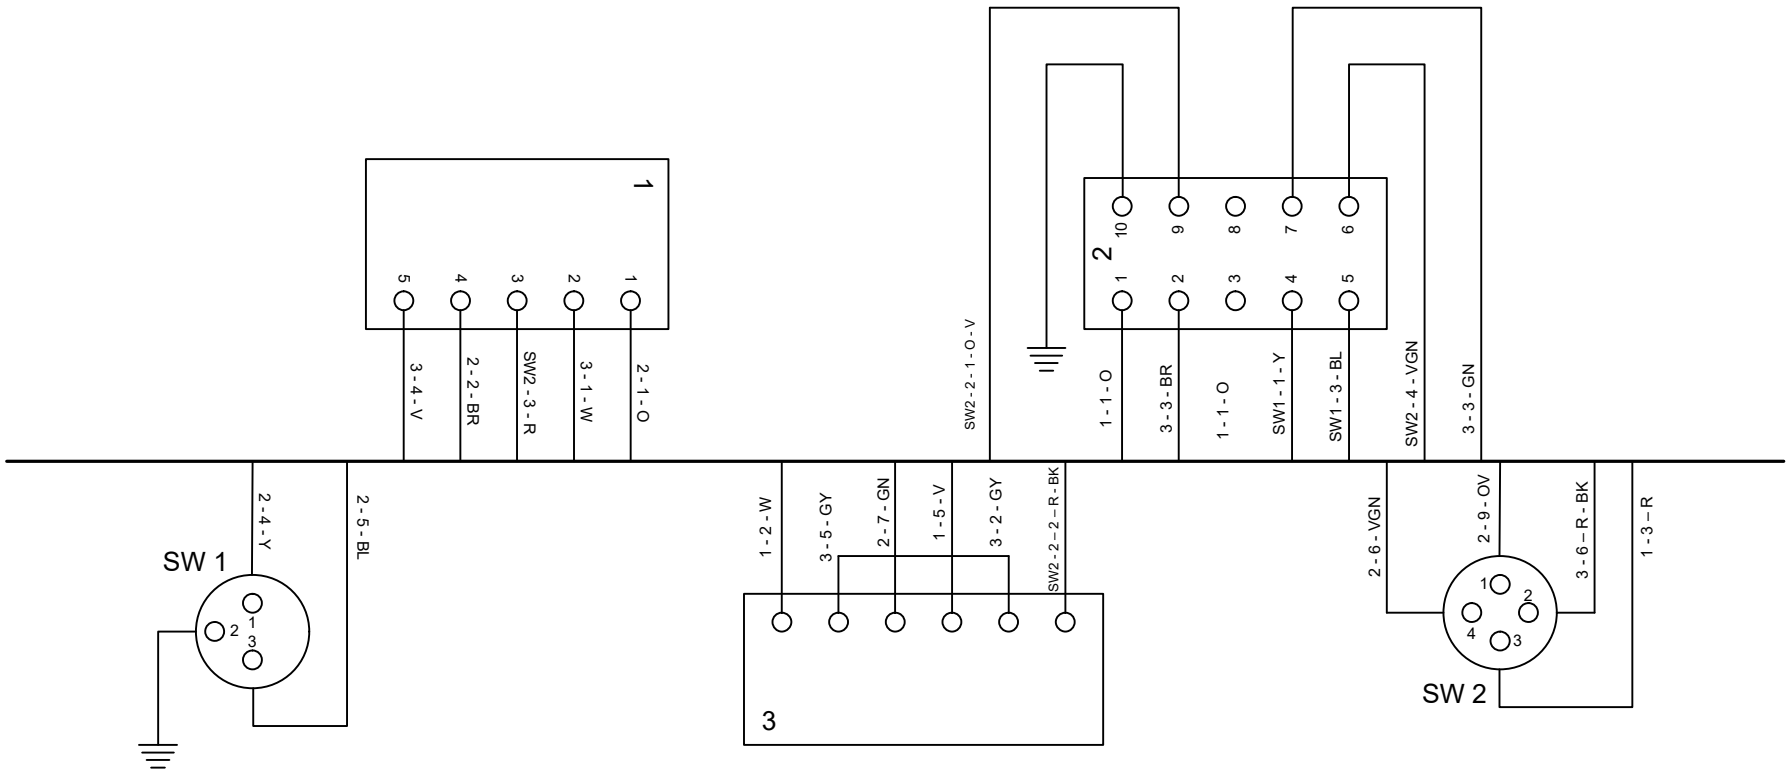


No.	
11	*DIAGRAM BASELINE*


Prodi D3 Teknik Telekomunikasi	Nama : Devita Syifa A	
	Kelas : 1A TTE	Tgl. 9-04-2023

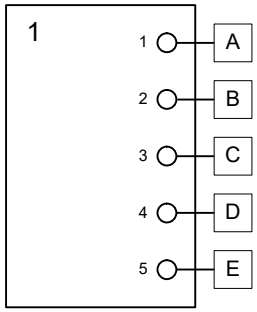


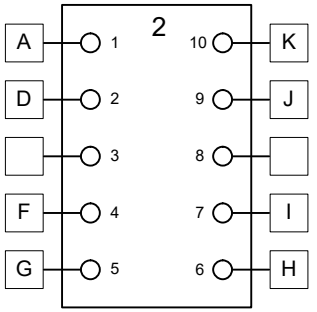

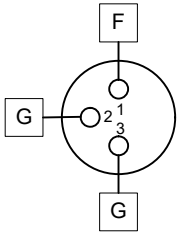

SW 1

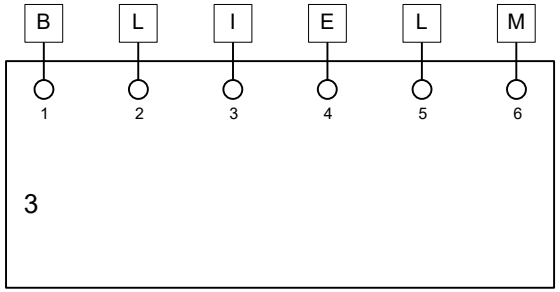

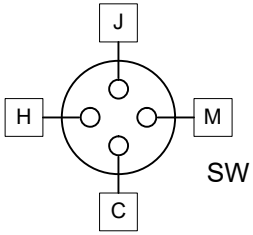

SW 2

WIRING TABLE			
WIRE I.D.	WIRE COLOR	FROM	TO
A	O	1-1	2-1
B	W	1-2	3-1
C	R	1-3	SW 2-3
D	BR	1-4	2-2
E	V	1-5	3-4
F	Y	2-4	SW 1-1
G	BL	2-5	SW 1-3
H	V-GN	2-6	SW 1-4
I	GN	2-7	3-3
J	0-V	2-9	SW 2-1
K	BK	2-10	GRD
L	GY	3-2	3-5
M	R-BK	3-6	SW 2-2
N	BK	SW 1-2	GRD

No. 11

DIAGRAM LINELESS

Prodi D3 Teknik Telekomunikasi

Nama : Devita Syifa A

Kelas : 1A TTE

Tgl. 9-04-2023